

機械器具装置図（屋外）　平面図 1/400

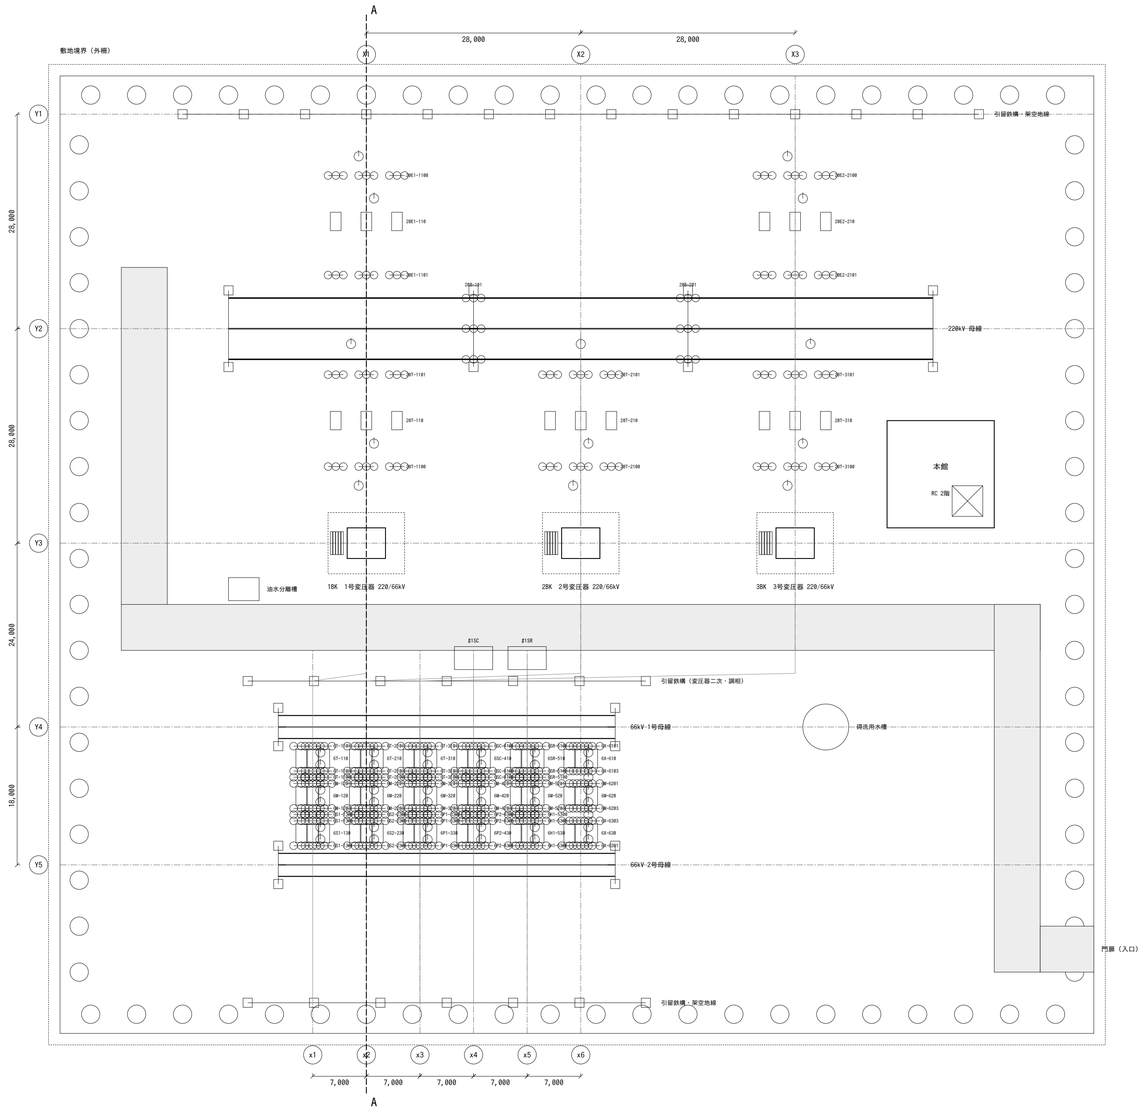

断面図　A－A（X1 通り、1BK を母線に垂直に切る。左が北）　1/400

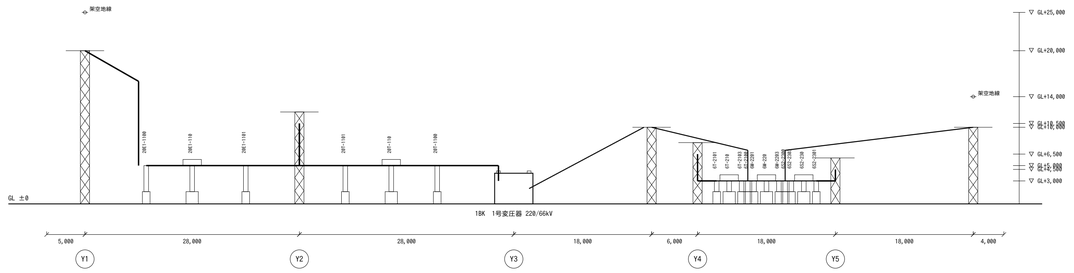

機械器具装置図	合成変電所
作成年月日　令和8年11月4日	図番　S-01-3
縮尺　1/400	
合成変電所（架空）。寸法・名称・番号はすべて仮定値	生成 synth/gen_drawings.py