記号は JIS C 0617 による。開閉器番号は記号の右、母線・線路は導体種別を併記。接地開閉器は区間ごとに記す。

単線結線図（主回路）

主要機器の概要（仮定値）

1BK・2BK・3BK　三相変圧器　220/66kV　製年 ―　製造者 ―

#1SC　電力用コンデンサ　66kV　　#1SR　分路リアクトル　66kV

母線形態　220kV 単母線（3 区間）　66kV 1・1/2 母線　　接地線　A種　軟銅より線

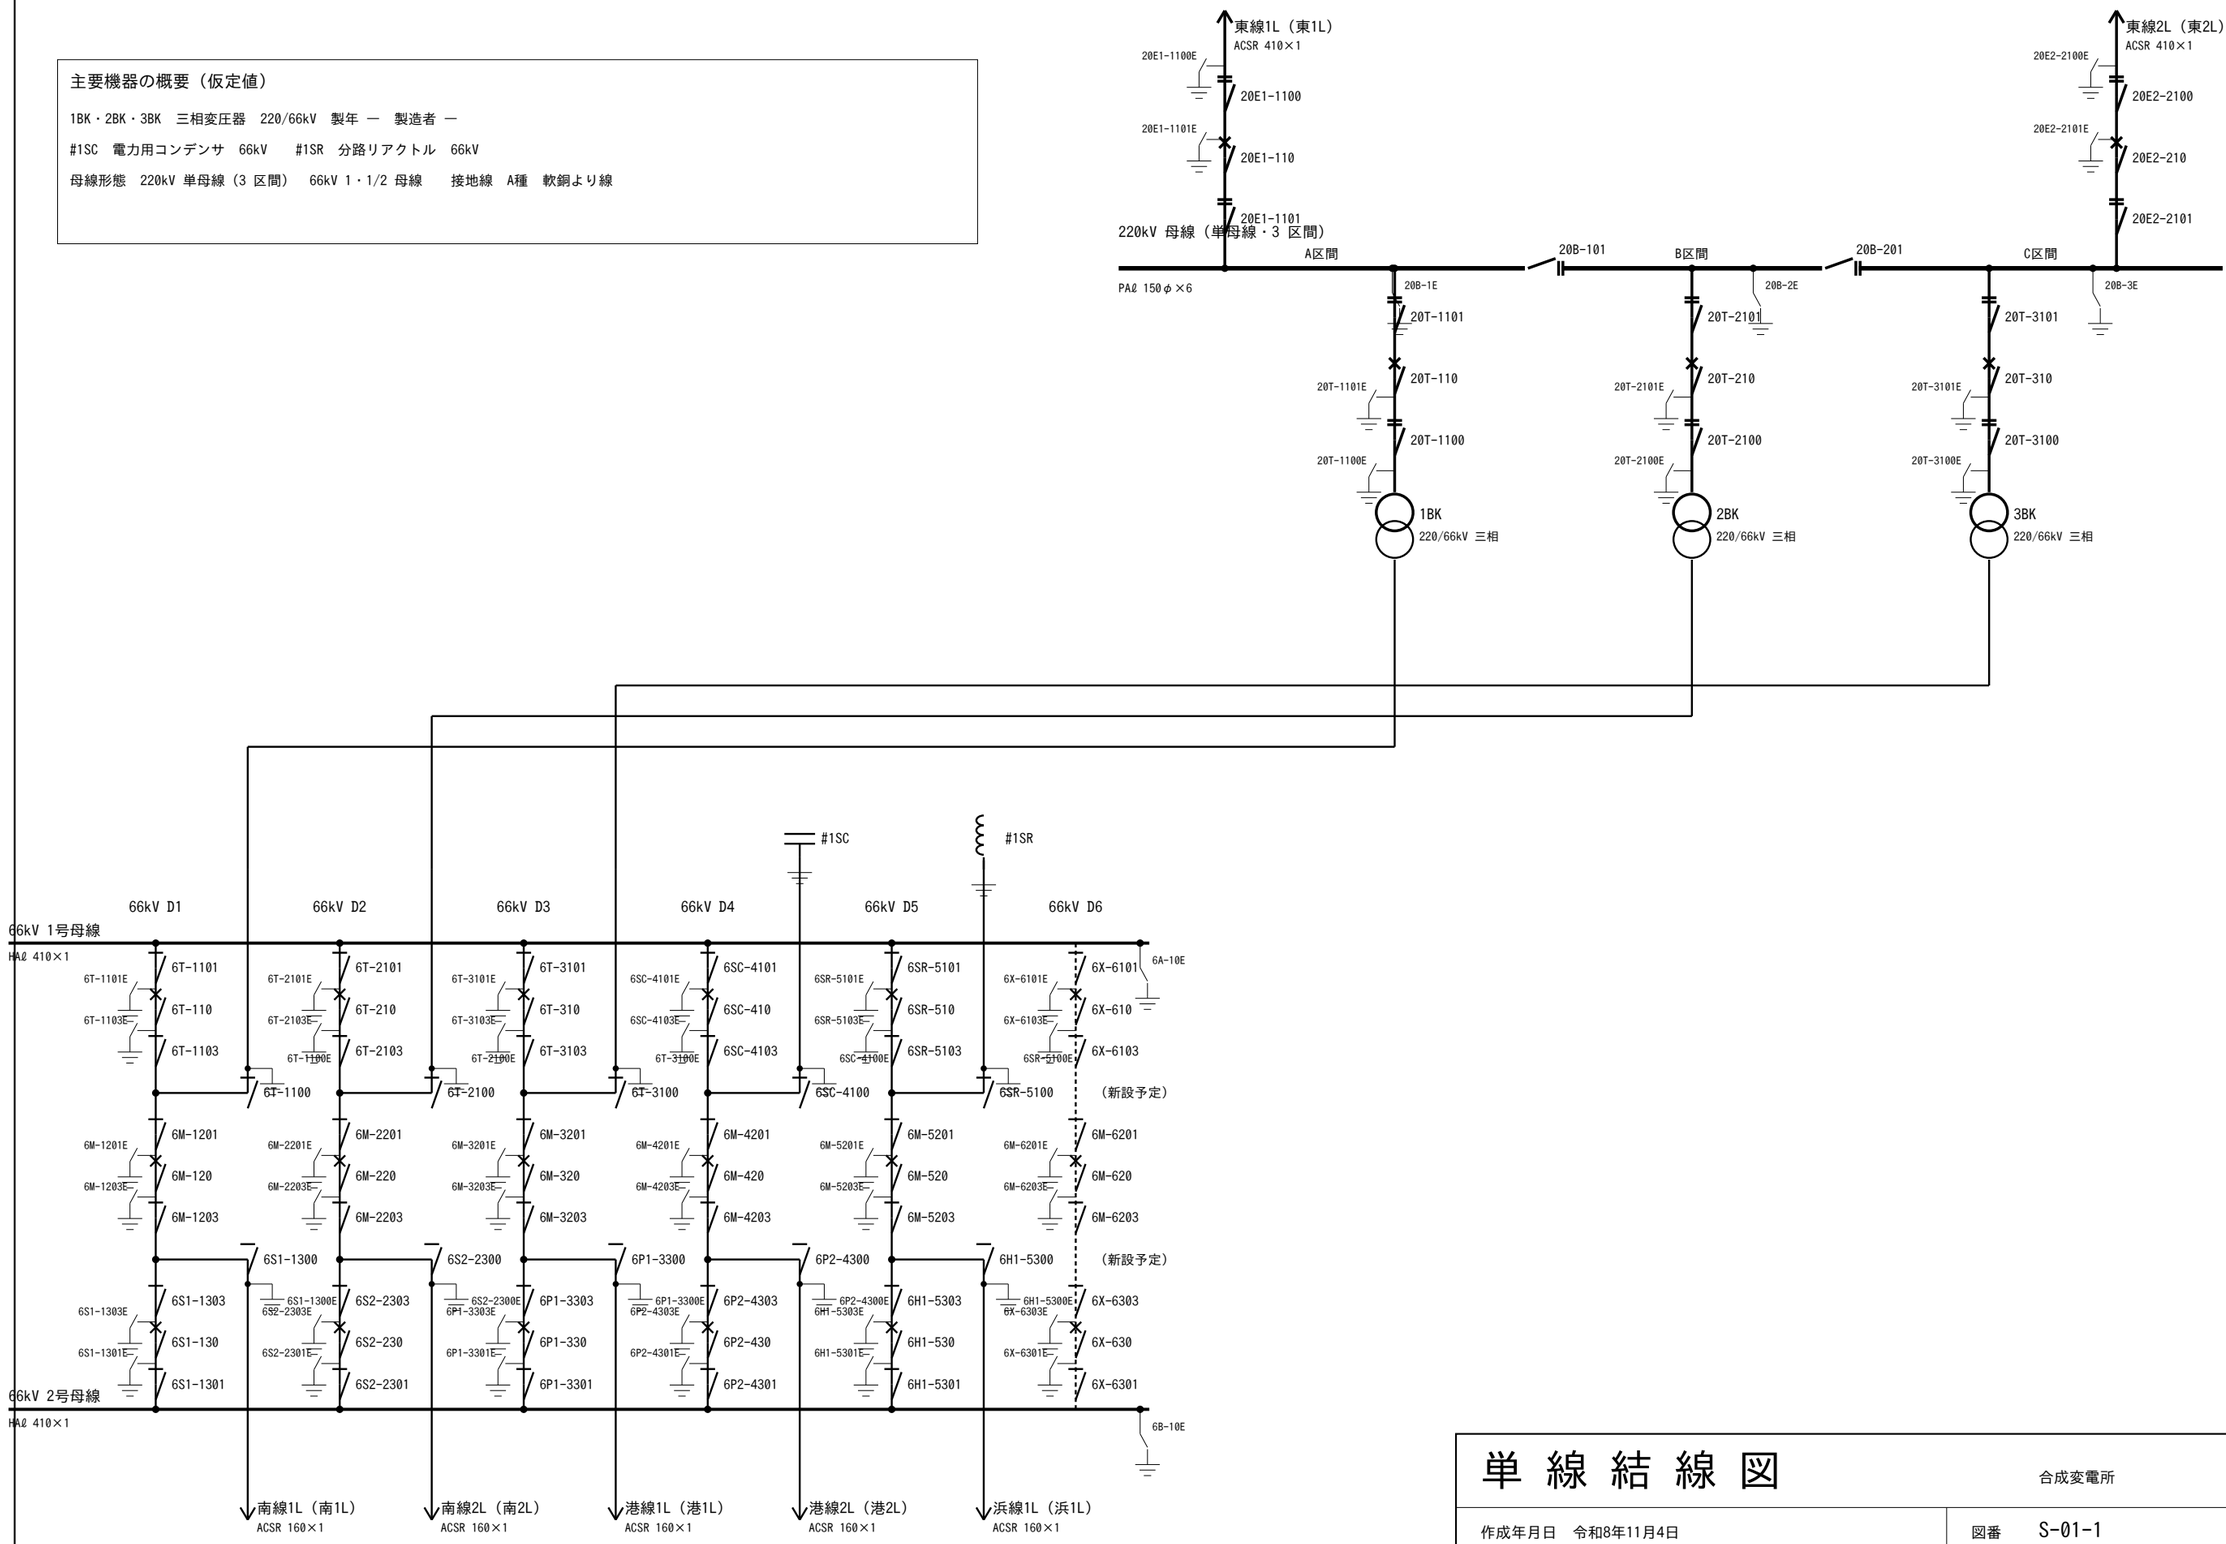

単 線 結 線 図

合成変電所

作成年月日　令和8年11月4日

縮尺　なし

合成変電所（架空）。寸法・名称・番号はすべて仮定値

図番　S-01-1

生成 synth/gen_drawings.py