機械器具装置図（屋外）　平面図 1/400

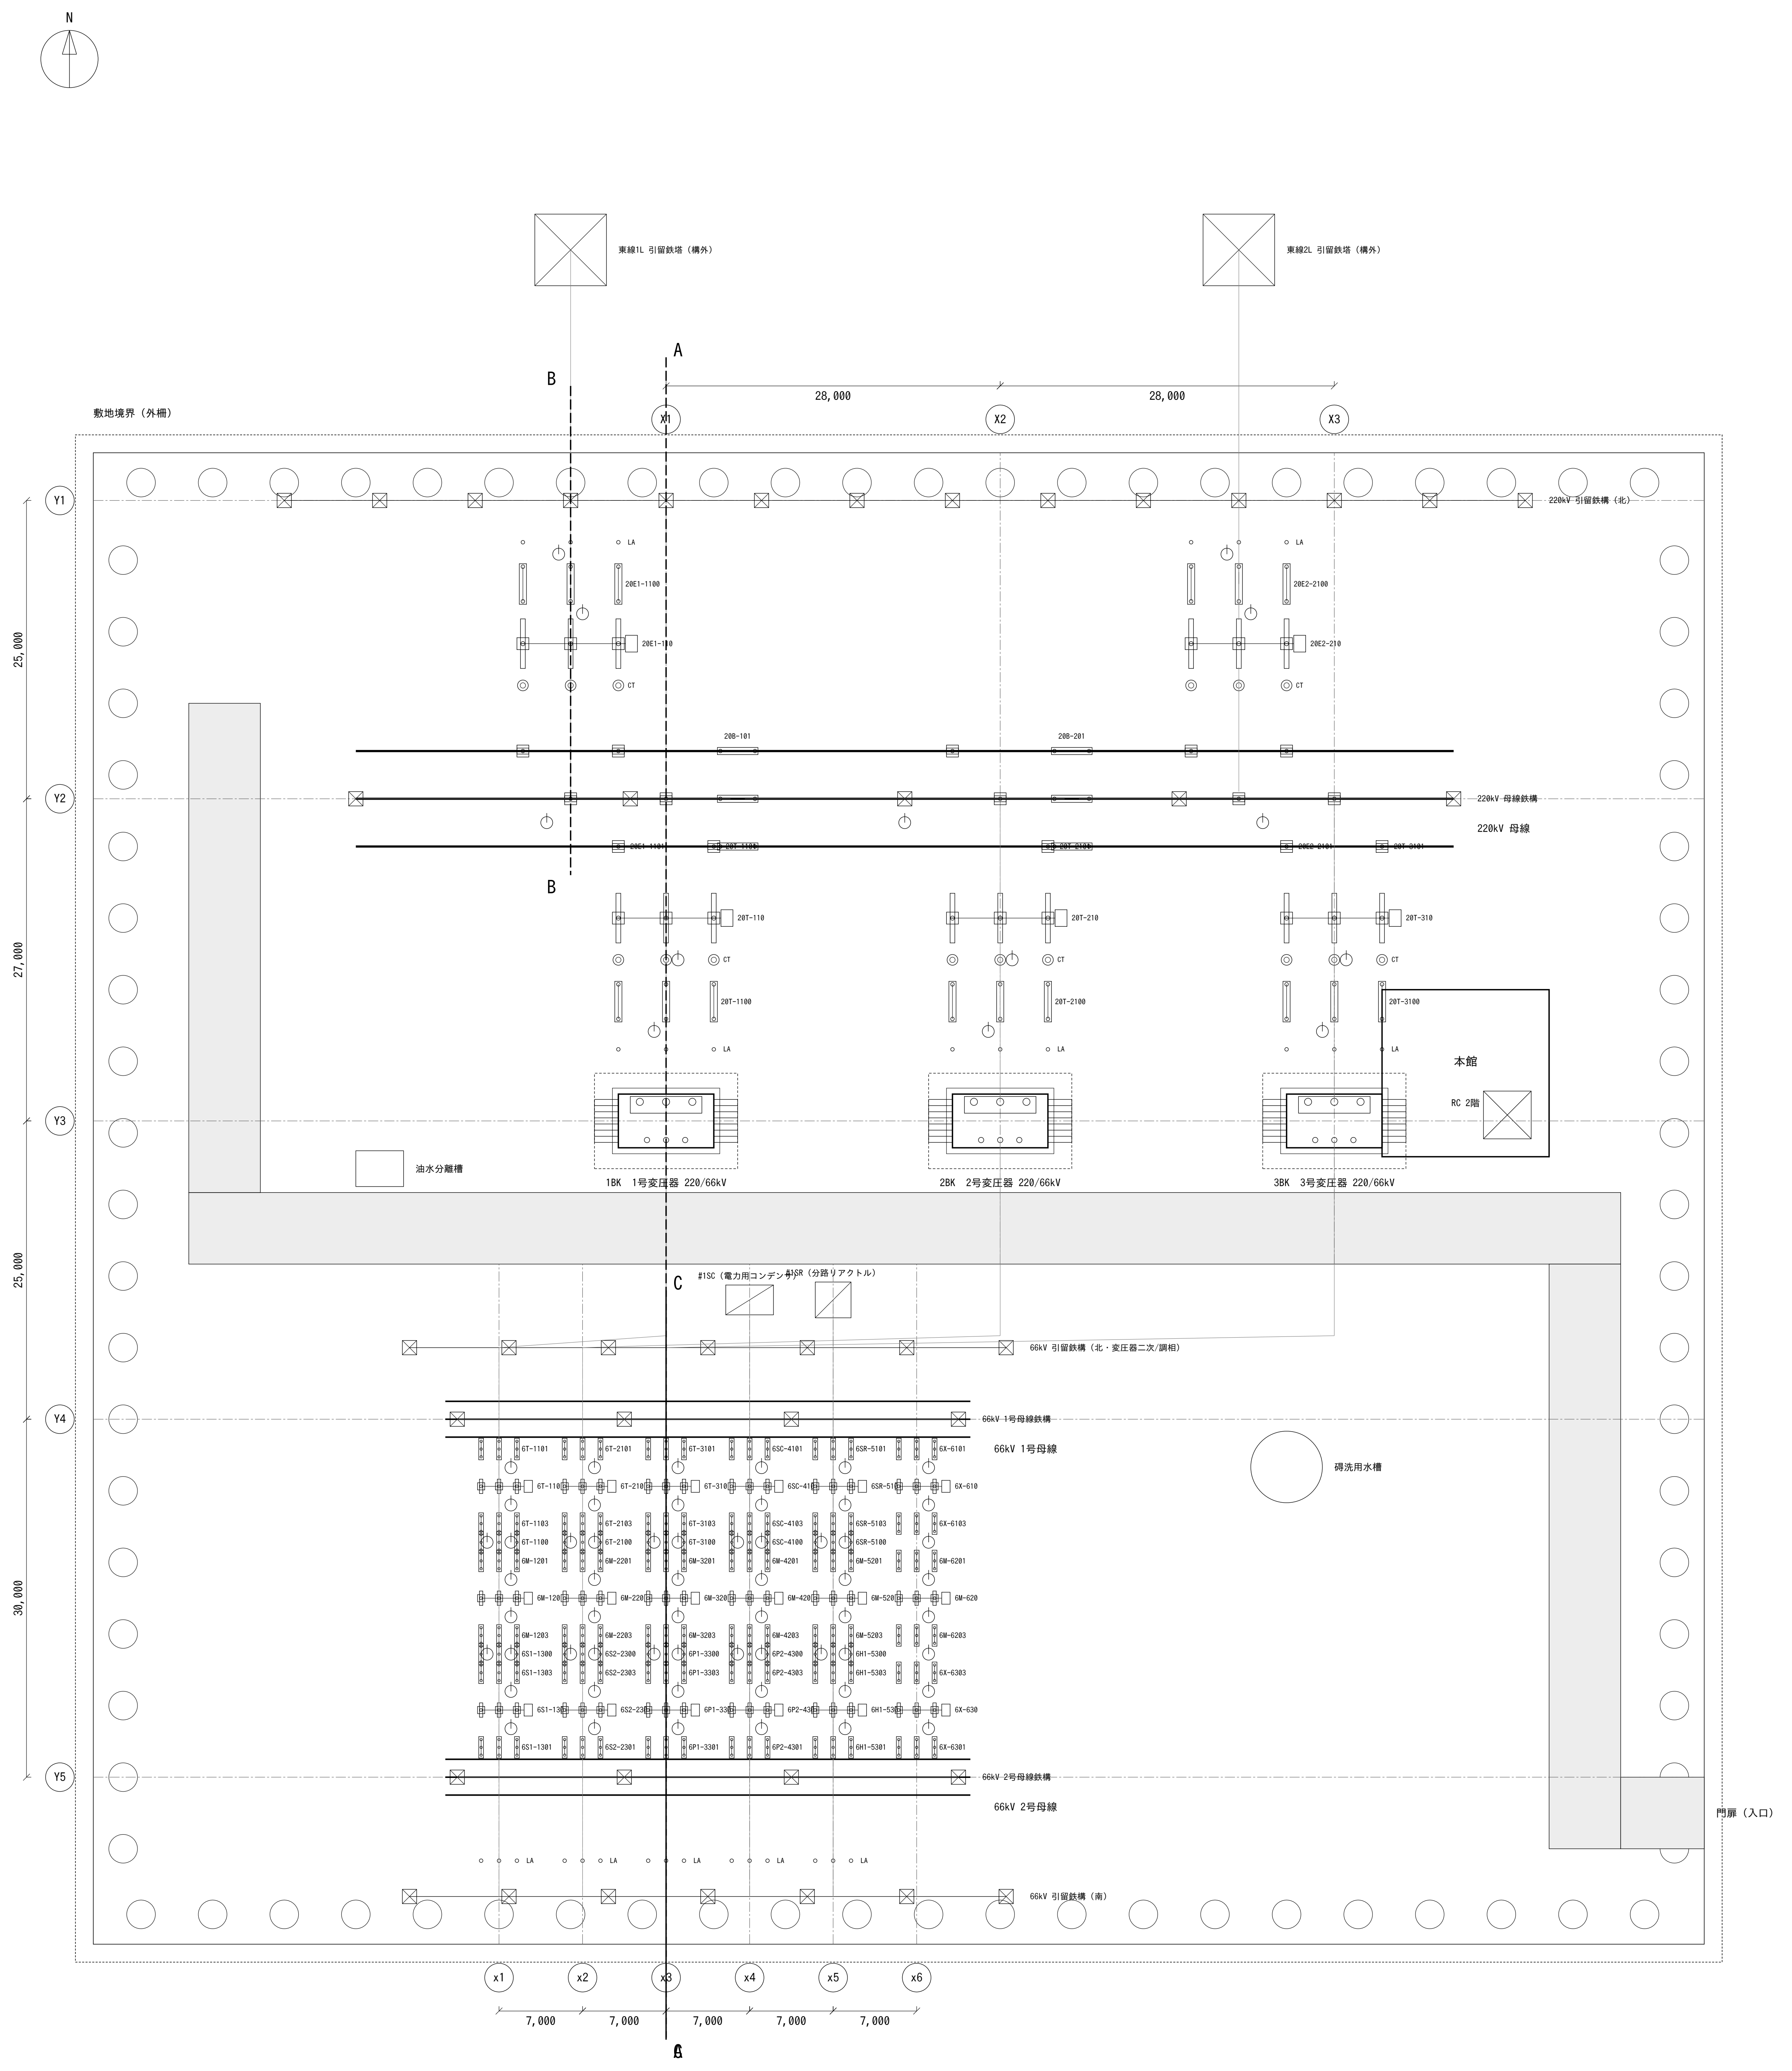
N
東線1L 引留鉄塔（構外）
東線2L 引留鉄塔（構外）
A
B
C
28,000
28,000
X1
X2
X3
敷地境界（外柵）
Y1
Y2
Y3
Y4
Y5
25,000
27,000
25,000
30,000
220kV 引留鉄構（北）
LA
20E1-1100
20E1-110
CT
20E2-2100
20E2-210
20B-101
20B-201
220kV 母線鉄構
220kV 母線
20E1-1101
20T-1101
20T-2101
20E2-2101
20T-3101
20T-110
20T-1100
20T-210
20T-2100
20T-310
20T-3100
本館
RC 2階
油水分離槽
1BK　1号変圧器 220/66kV
2BK　2号変圧器 220/66kV
3BK　3号変圧器 220/66kV
#1SC（電力用コンデンサ）
#1SR（分路リアクトル）
66kV 引留鉄構（北・変圧器二次/調相）
66kV 1号母線鉄構
66kV 1号母線
6T-1101
6T-2101
6T-3101
6SC-4101
6SR-5101
6X-6101
6T-110
6T-210
6T-310
6SC-410
6SR-510
6X-610
6T-1103
6T-2103
6T-3103
6SC-4103
6SR-5103
6X-6103
6T-1100
6T-2100
6T-3100
6SC-4100
6SR-5100
6M-1201
6M-2201
6M-3201
6M-4201
6M-5201
6M-6201
6M-120
6M-220
6M-320
6M-420
6M-520
6M-620
6M-1203
6M-2203
6M-3203
6M-4203
6M-5203
6M-6203
6S1-1300
6S2-2300
6P1-3300
6P2-4300
6H1-5300
6S1-1303
6S2-2303
6P1-3303
6P2-4303
6H1-5303
6X-6303
6S1-130
6S2-230
6P1-330
6P2-430
6H1-530
6X-630
6S1-1301
6S2-2301
6P1-3301
6P2-4301
6H1-5301
6X-6301
66kV 2号母線鉄構
66kV 2号母線
碍洗用水槽
門扉（入口）
66kV 引留鉄構（南）
x1
x2
x3
x4
x5
x6
7,000
7,000
7,000
7,000
7,000

断面図　A－A（X1 通り。1BK のベイを母線に垂直に切る。左が北）　1/400

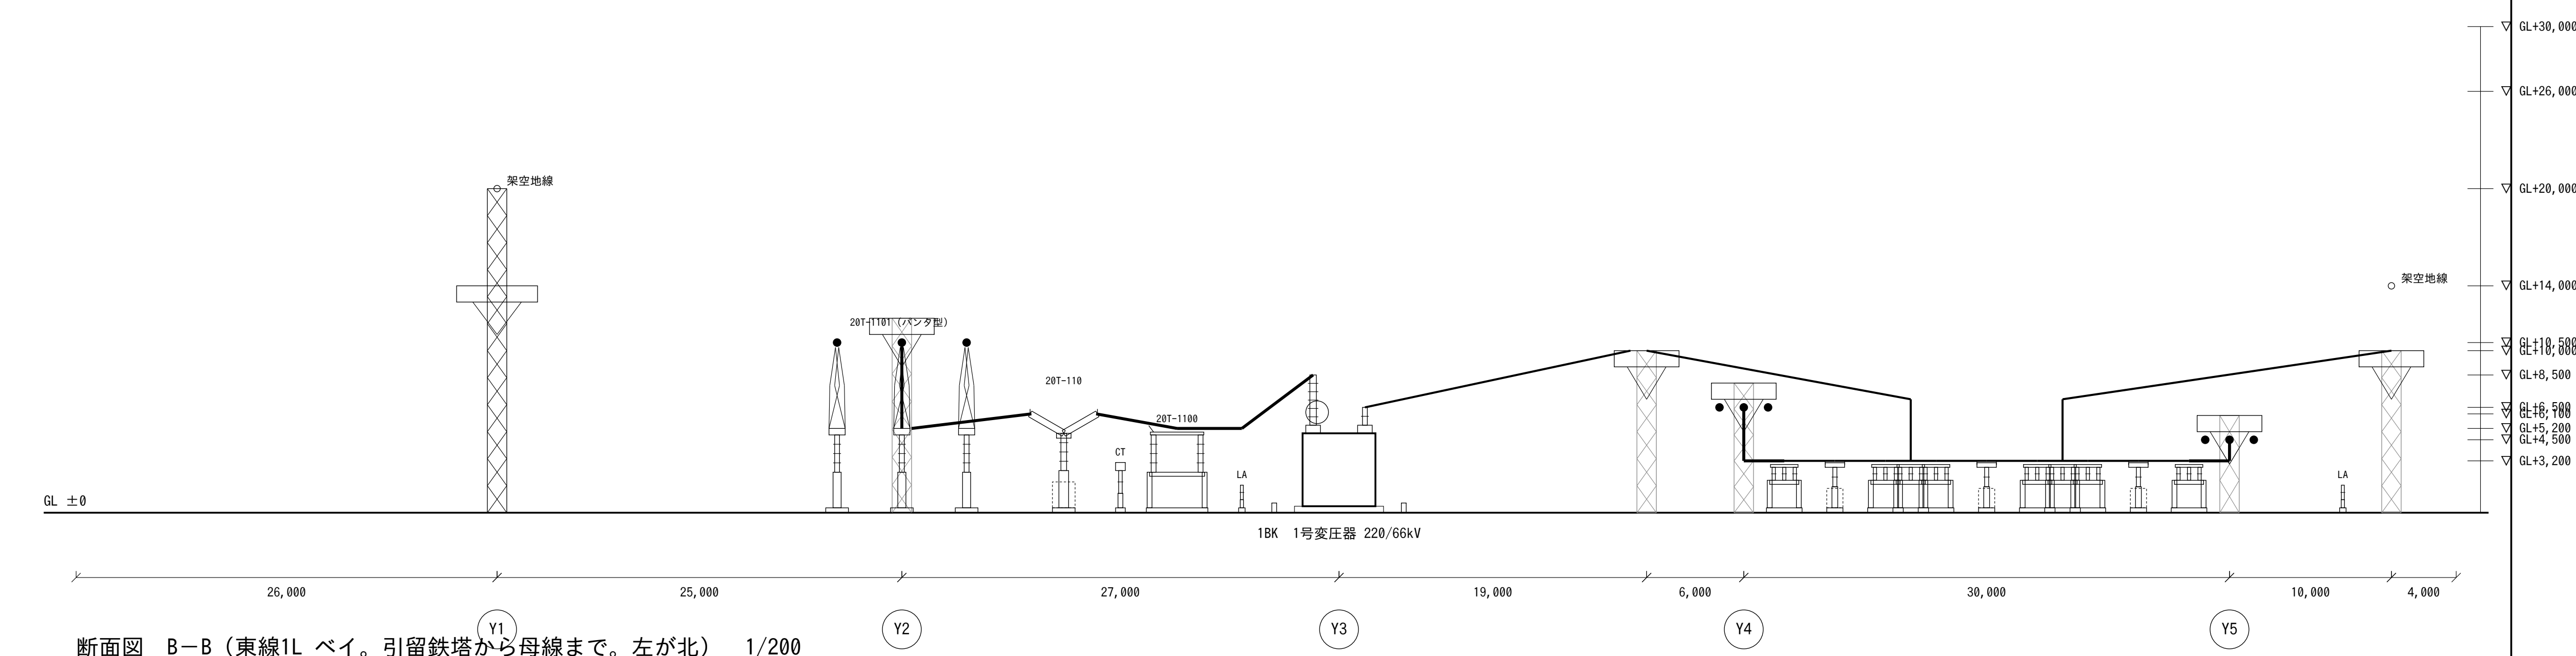
架空地線
20T-1101（パンタ型）
20T-110
20T-1100
CT
LA
GL ±0
1BK　1号変圧器 220/66kV
26,000
25,000
27,000
19,000
6,000
30,000
10,000
4,000
Y1
Y2
Y3
Y4
Y5
架空地線
GL+30,000
GL+26,000
GL+20,000
GL+14,000
GL+10,500
GL+10,000
GL+8,500
GL+6,500
GL+6,100
GL+5,200
GL+4,500
GL+3,200

断面図　B－B（東線1L ベイ。引留鉄塔から母線まで。左が北）　1/200

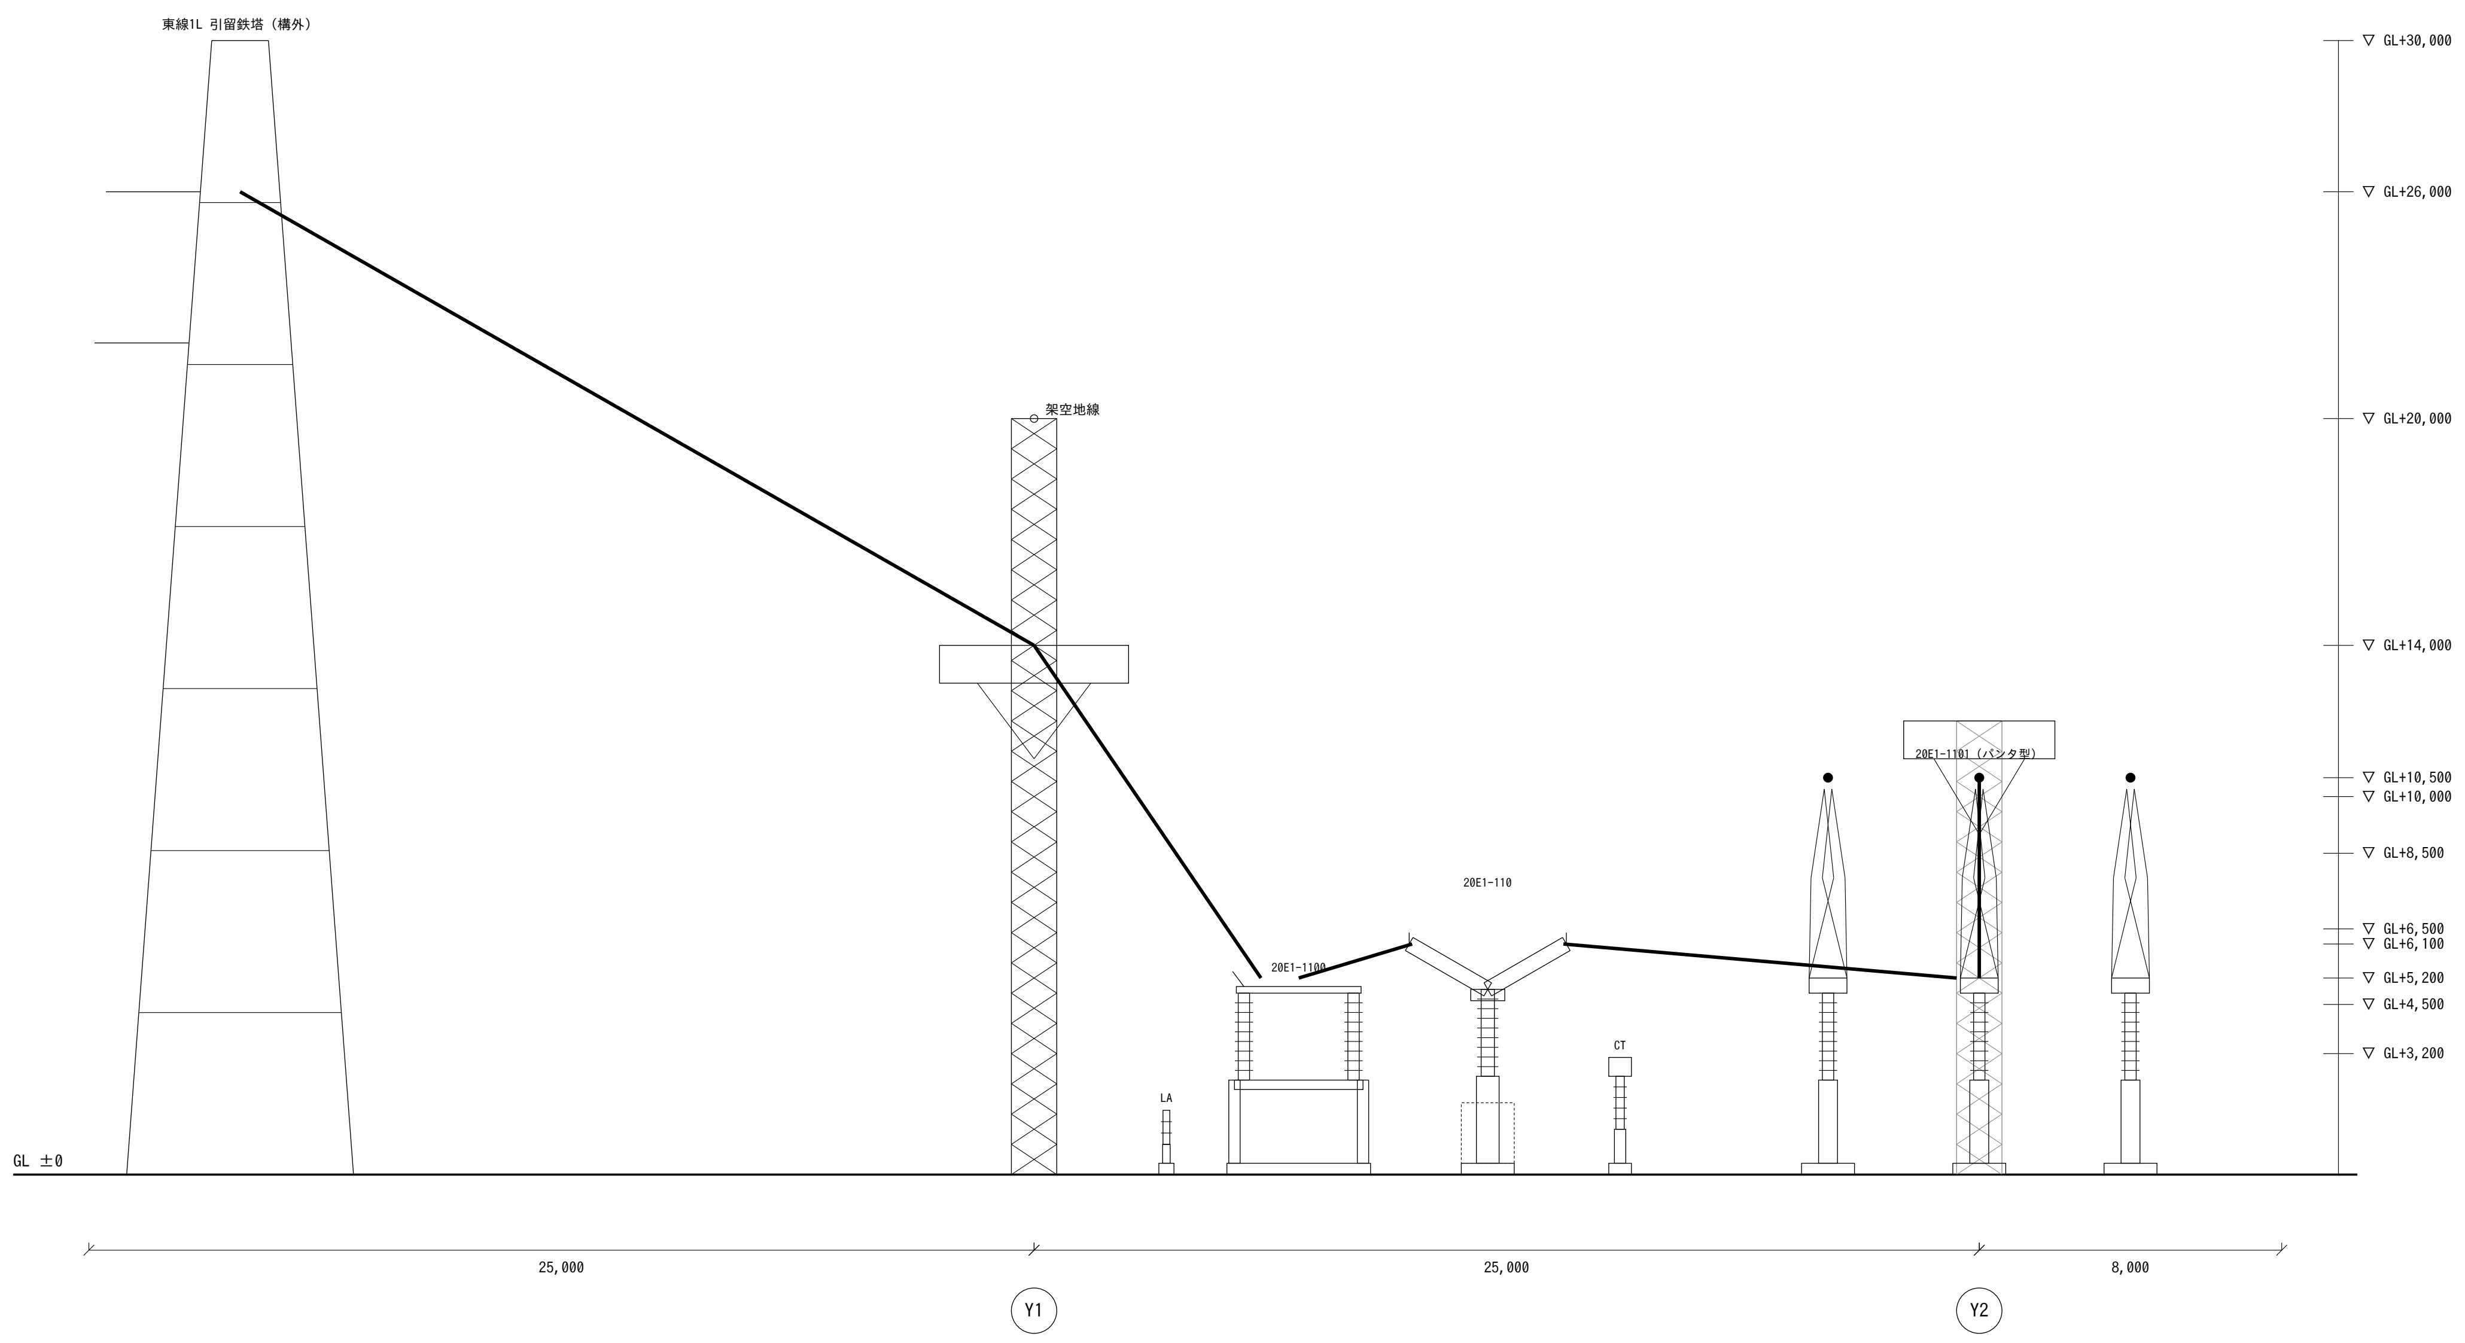
東線1L 引留鉄塔（構外）
架空地線
20E1-1100
20E1-110
CT
LA
20E1-1101（パンタ型）
GL ±0
GL+30,000
GL+26,000
GL+20,000
GL+14,000
GL+10,500
GL+10,000
GL+8,500
GL+6,500
GL+6,100
GL+5,200
GL+4,500
GL+3,200
25,000
25,000
8,000
Y1
Y2

断面図　C－C（X1 通り。66kV ダイヤ D3 を母線に垂直に切る。左が北）　1/200

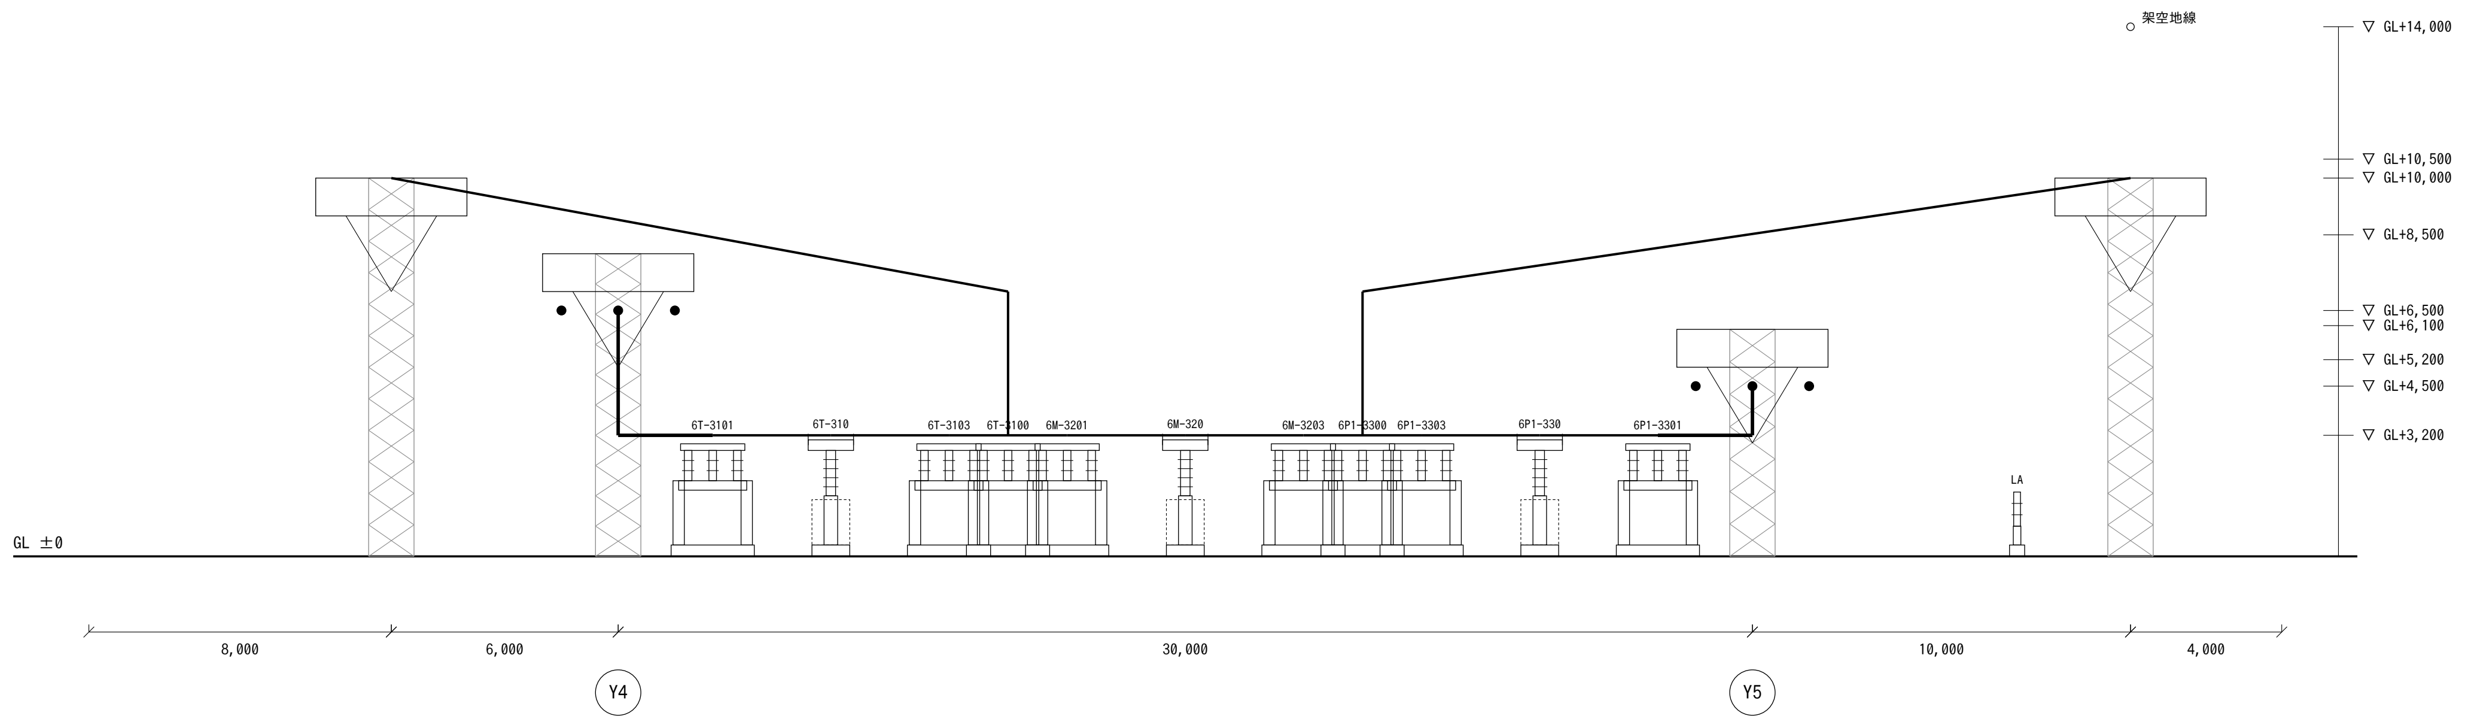
架空地線
GL+14,000
GL+10,500
GL+10,000
GL+8,500
GL+6,500
GL+6,100
GL+5,200
GL+4,500
GL+3,200
6T-3101
6T-310
6T-3103
6T-3100
6M-3201
6M-320
6M-3203
6P1-3300
6P1-3303
6P1-330
6P1-3301
LA
GL ±0
8,000
6,000
30,000
10,000
4,000
Y4
Y5

機 械 器 具 装 置 図

合成変電所

作成年月日　令和8年11月4日
縮尺　1/400
合成変電所（架空）。寸法・名称・番号はすべて仮定値

図番　S-01-3

生成 synth/gen_drawings.py